ANNA KRASH 2026



PORTFOLIO

ПРИВЕТ!



Анна Крашенинникова

Креативный архитектор

24 года · магистр архитектуры · 5 лет опыта

Контакты

+7 999 623 68 48

annkrash@gmail.com

Москва, Россия

Программы

- ArchiCAD
- Autodesk Revit
- Adobe Photoshop
- Figma
- Lumion
- QGIS

Языки

Русский - родной

Английский - B1

Интересы

Архитектурная графика

анимация

GameDev

путешествия

Портфолио

Яндекс диск

В работе ценю выразительную концепцию, точность композиции, внимание к деталям Специализируюсь на быстром выполнении поставленного ТЗ, поиске визуального образа проекта, графической подаче, координации визуализаторов и архитекторов

Образование

2024 - 2026 · г. Уфа, Россия

Магистр архитектуры

Уфимский государственный нефтяной технический университет, архитектурно-строительный факультет

06.2023 - 07.2023 · г.Санкт-Петербург, Россия

Преддипломная практика

Прохождение практики в архитектурном бюро "Студия 44"

06.2022 - 07.2022 · г. Уфа, Россия

Производственная практика

Прохождение практики в архитектурном бюро "Ахмадуллин архитектс"

2019 - 2024 · г. Уфа, Россия

Бакалавр архитектуры

Уфимский государственный нефтяной технический университет, архитектурно-строительный факультет

2012 - 2015 · г. Уфа, Россия

Доп. художественное образование

Художественная школа №1 им А. Кузнецова

Опыт работы

09.2024 - 07.2026 · 1 год 11 месяцев

Креативный архитектор

PERGAEV BUREAU · Архитектура и проектирование

09.2020 - 05.2024 · 3 года 9 месяцев

Архитектор-дизайнер


Фриланс · Частная практика

Профессиональные достижения

- **Диплом I степени**
  XXVI международный форум «Новые идеи нового века – 2026» в номинации «Архитектура» за проект «Реконструкция квартала № 420 в г. Уфе», 2026.
- **Диплом III степени**
  Международный фестиваль «Дни архитектуры» в номинации «Студенческие работы», категория «Дипломные работы», за проект по реновации территории , 2026.
- **Первый приз**
  Китайско-российский студенческий конкурс на эскиз-идею по градостроительному и архитектурному проектированию, 2024.
- **Финалист и обладатель специального приза**
  Международный архитектурный конкурс Saint-Gobain, 2024.
- **Первое место**
  XXIII международный форум «Новые идеи нового века» в номинации «Архитектурный рисунок», 2023.
- **Второе место**
  XXII международный форум «Новые идеи нового века» в номинации «Архитектурный рисунок», 2022.
- **Первое место**
  Межрегиональный молодёжный форум развития территорий «Городские реновации 2.0» в номинации «Концепция развития кампуса УГНТУ», 2021.

СОДЕРЖАНИЕ

01

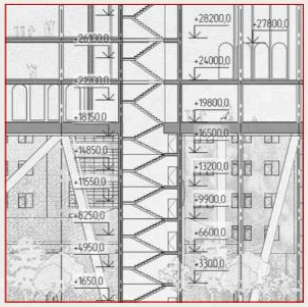

СТАДИЯ АР

02 03




КОЛЛАЖНЫЕ ПОДАЧИ

04




ВИЗУАЛИЗАЦИИ

05

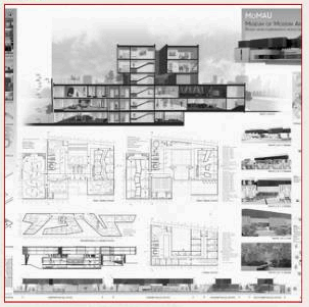

ПОДАЧА ПОДРАМНИКА

06

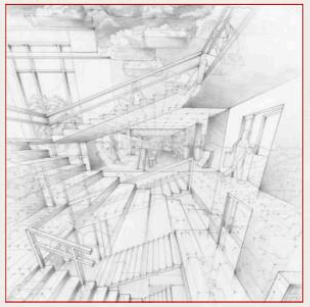

АРХИТЕКТУРНЫЙ РИСУНОК

стадия АР

схемы, планировочные решения, фасады, разрезы и прочие графические составляющие проектно-рабочей документации.


В портфолио будут представлены следующие примеры графических работ:

1. планировочные решения;
2. схема-аксонометрия;
3. разрезы;
4. фасады;
5. генеральный план.

(1)



ПЛАНИРОВОЧНЫЕ РЕШЕНИЯ

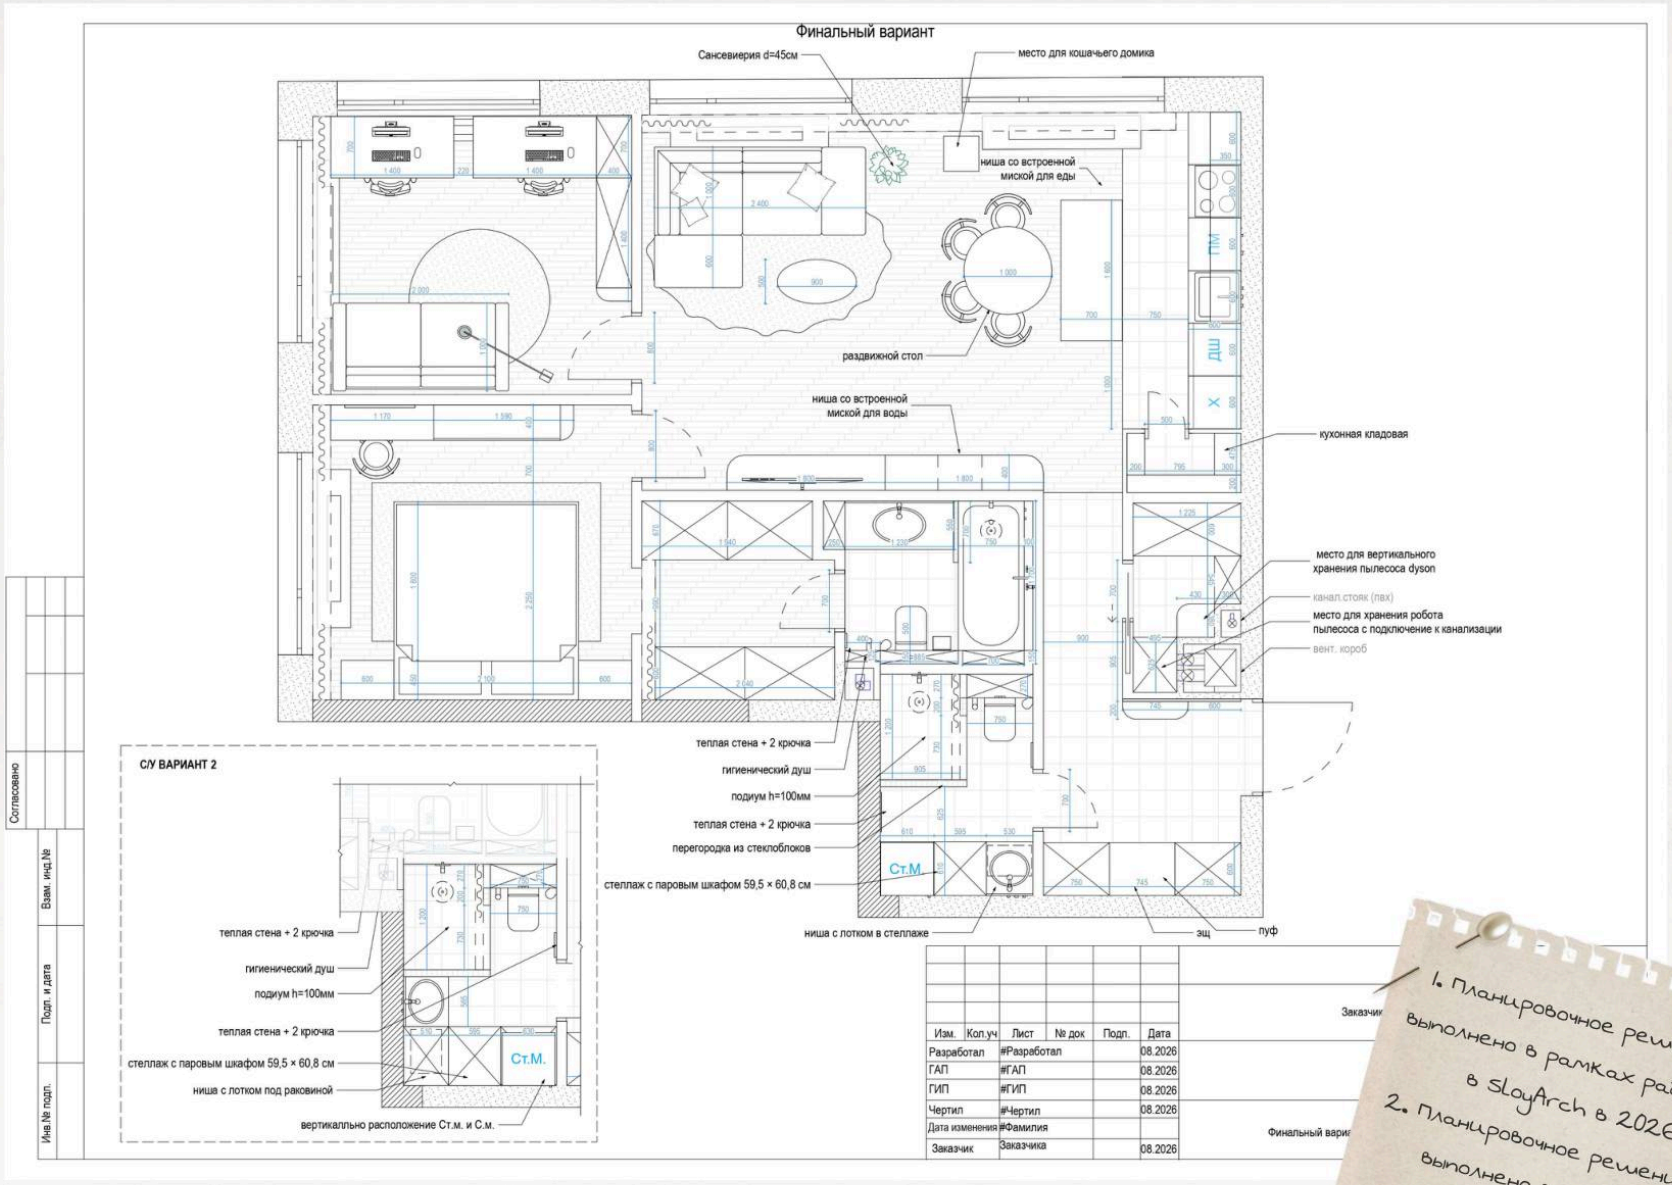


1. Планировочное решение выполнено в рамках работы в SlayArch в 2026 г.
2. Планировочное решение выполнено в программе Archicad

ФУНКЦИОНАЛЬНАЯ СХЕМА

1. Схемы выполнены в рамках работы в Pergaev Bureau в 2026 г.
2. Схемы выполнены в программе Revit


Условные обозначения:

- 1 Хамам
- 2 Зал йоги
- 3 Спорт-зал
- 4 Сауна
- 5 Раздевалка
- 6 Душевые
- 7 С/У
- 8 Спа-зона
- Лестничная клетка
- Лифт

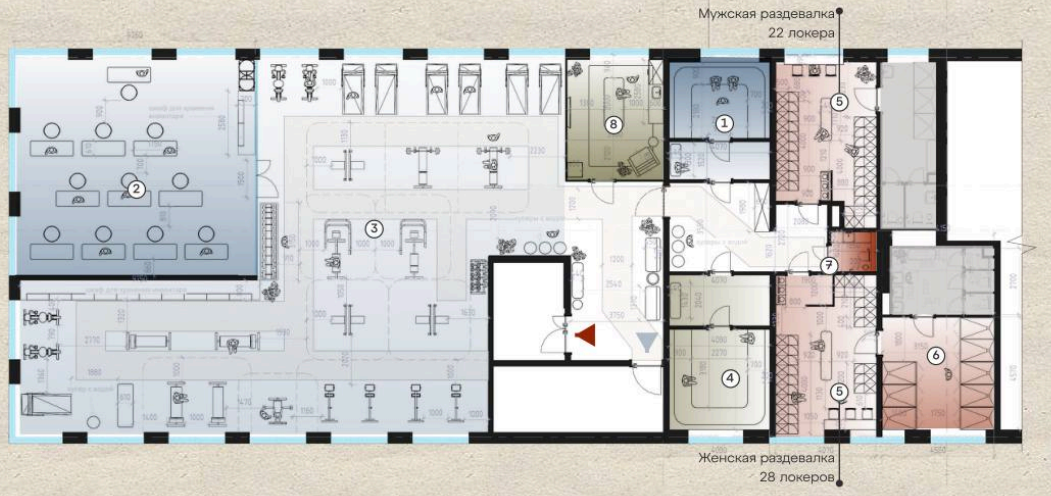

Условные обозначения:

- Хамам
- Зал йоги
- Спорт-зал
- Сауна
- Раздевалка
- Душевые
- С/У
- Спа-зона

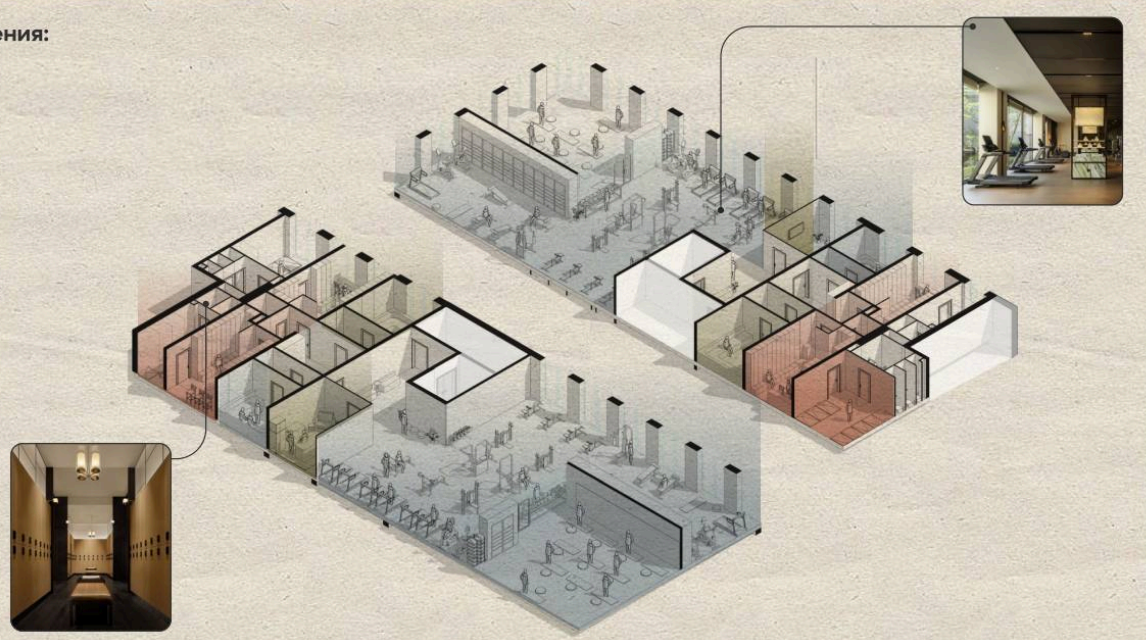



ВЗРЫВ-СХЕМА

Вариант оформления
аксонометрий
в коллажной подаче



РАЗРЕЗЫ

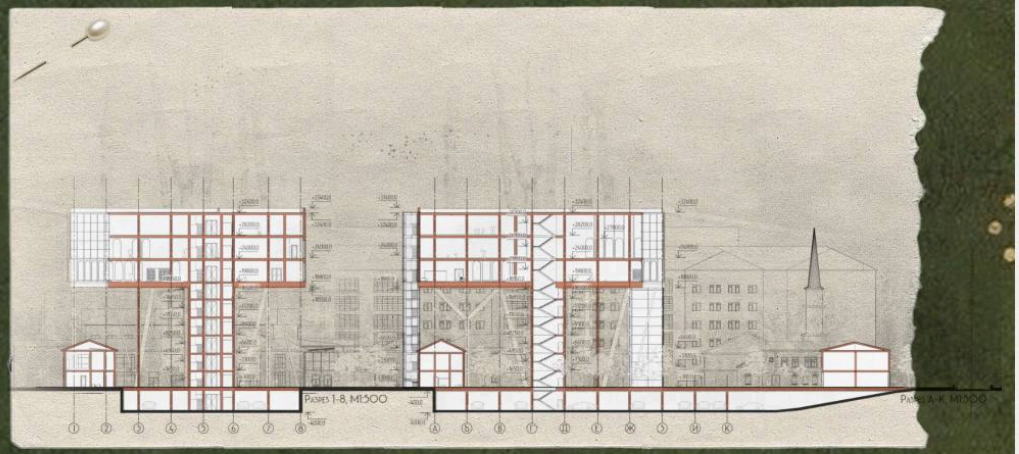


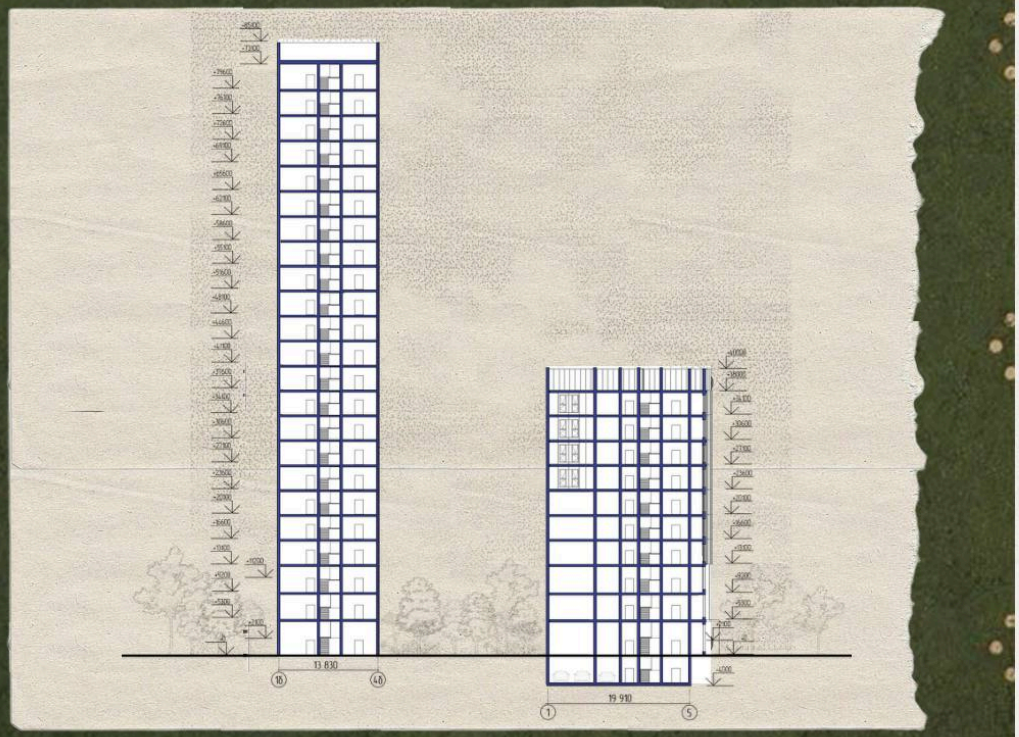

1. Разрезы выполнены в рамках КП на бакалавриате в 2024 г.
2. Разрезы выполнены в программах ArchiCad + Adobephotoshop

ФАСАДЫ

1. Фасады выполнены в рамках КП на бакалавриате в 2024 г.
2. Фасады выполнены в программах ArchiCad + AbobePhotoshop

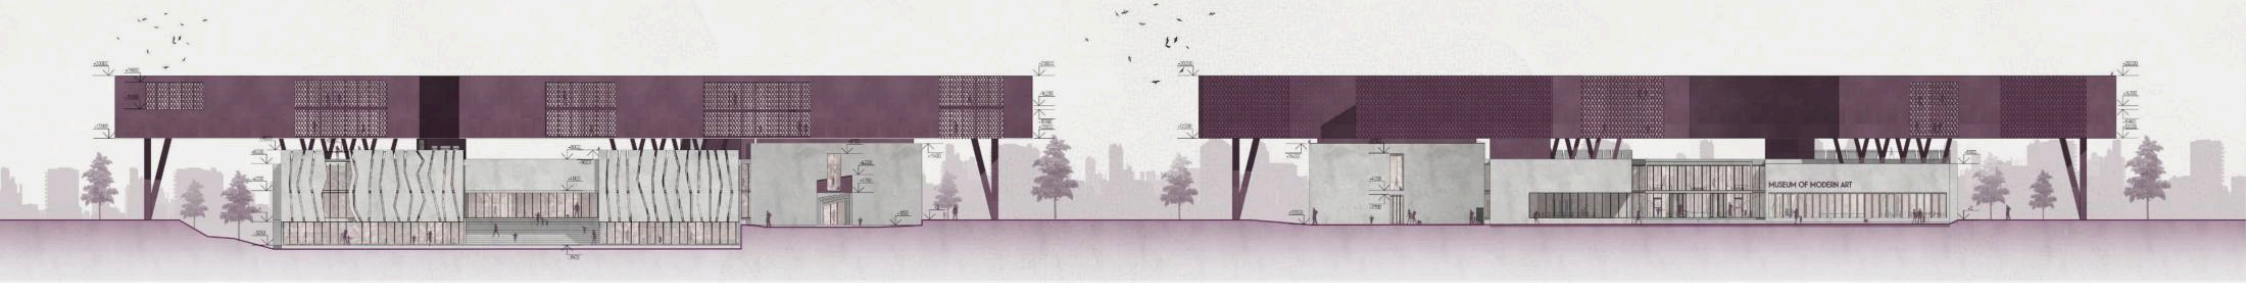



Развертка по ул. Мусы Карима, М1:500


Фасад 3-А, М1:500

Фасад 8-1, М1:500

НАУЧНЫЙ РУКОВОДИТЕЛЬ: УСОВА А.В.
ВЫПОЛНИЛ: СТ. УГНТУ, РОССИЯ КРАШЕНИННИКОВА А. А.

ГЕНЕРАЛЬНЫЙ ПЛАН

1. Генплан выполнен в рамках бакалаврской дипломной работы в 2024 г.
2. Генплан выполнен в программах ArchiCad + AbobePhotoshop

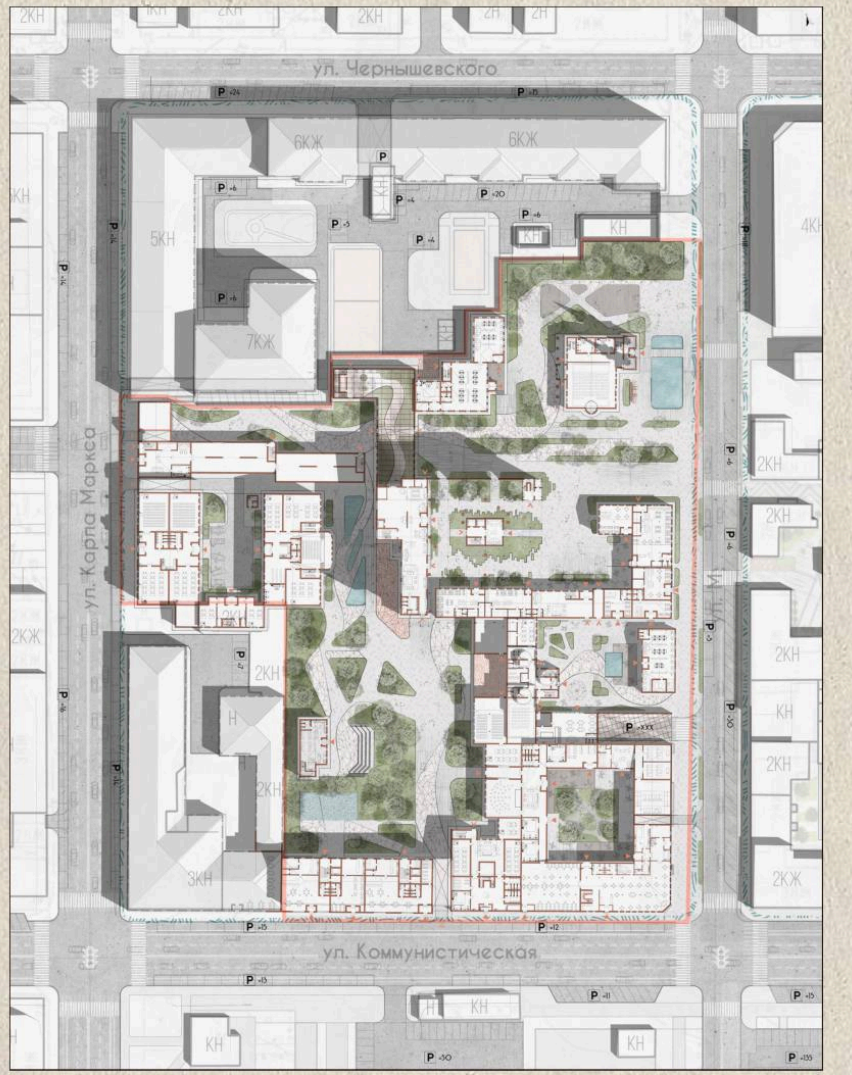


КОЛЛАЖ КАК МУДБОРД

СБОРКА МУДБОРДА С ПОЗИЦИЯМИ ИЗ ЗАКУПА С ЦЕЛЬЮ ПОКАЗАТЬ ЗАКАЗЧИКУ ОБРАЗ БУДУЩЕГО ИНТЕРЬЕРА

(2)



КОЛЛАЖ КАК МУДЬОРД

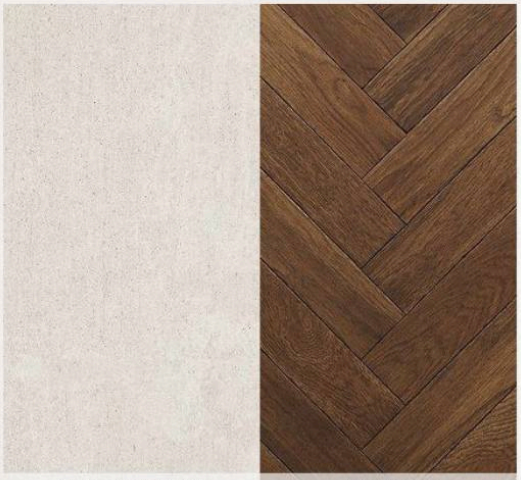

ДЕКОРАТИВНАЯ ШТКАТУРКА

ПАРКЕТНАЯ ДОСКА



ПЛИТКА С ДЕКОРАТИВНЫМИ ВСТАВКАМИ



КЕРАМОГРАНИТ ПОД МАРФИЛ



Вариант подачи мудборда с подбором отделки. На месте отделки могут быть закупные позиции мебели, света или декора

КОЛЛАЖ КАК МУДБОРД

Вариант подачи мудборда
без подбора аналогов




КОЛЛАЖ КАК ТЗ ВИЗУАЛИЗАТОРУ

БЫСТРЫЙ НАБРОСОК ИДЕИ, С ЦЕЛЬЮ ПОКАЗАТЬ ВИЗУАЛИЗАТОРУ БУДУЩИЙ ОБРАЗ ПРОСТРАНСТВА И ВЫДАТЬ ТЗ НА ЕГО ОСНОВЕ С ПРИКРЕПЛЕНИЕМ ССЫЛОК НА ЗАКУП И ГАБАРИТОВ КОНСТРУКЦИЙ


(3)



КОЛЛАЖ КАК ТЗ ВИЗУАЛИЗАТОРУ

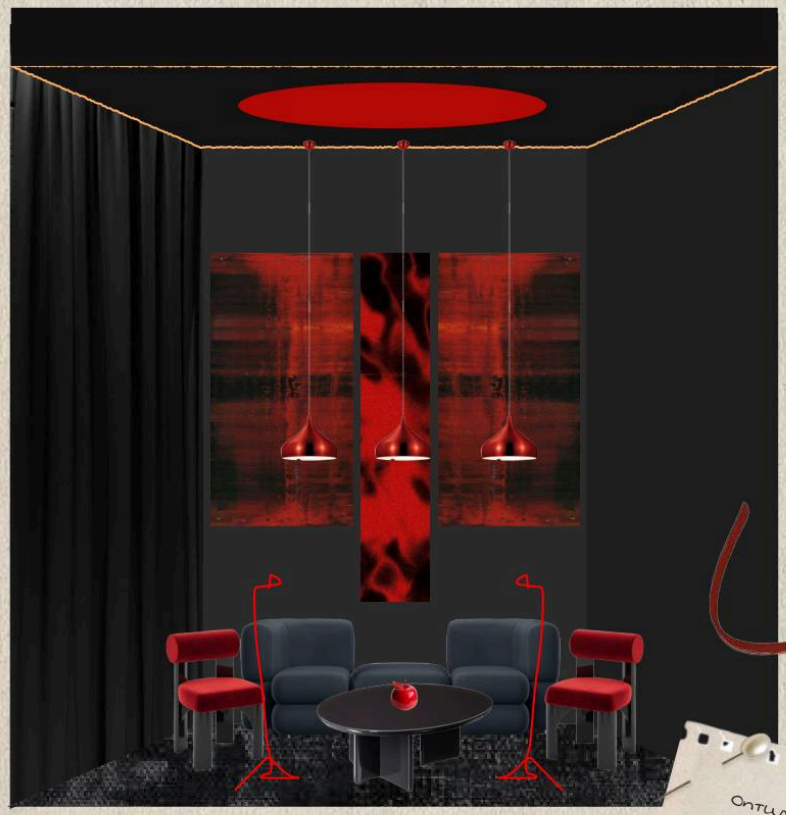



Оптимальный вариант выдачи ТЗ с привязками закупных позиций и подходящих текстур

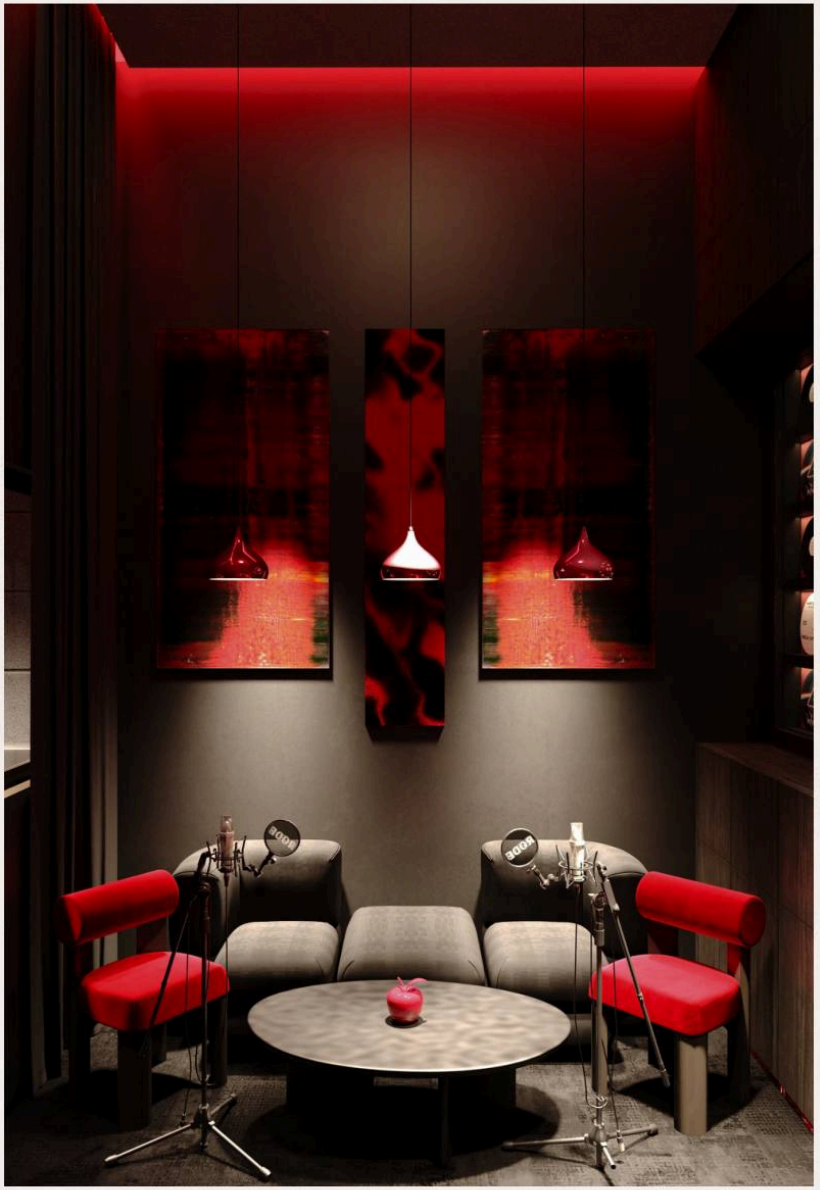


*Визуализация выполнена визуализаторами в рамках работы над проектом в Pergaev Bureau в 2026 г.



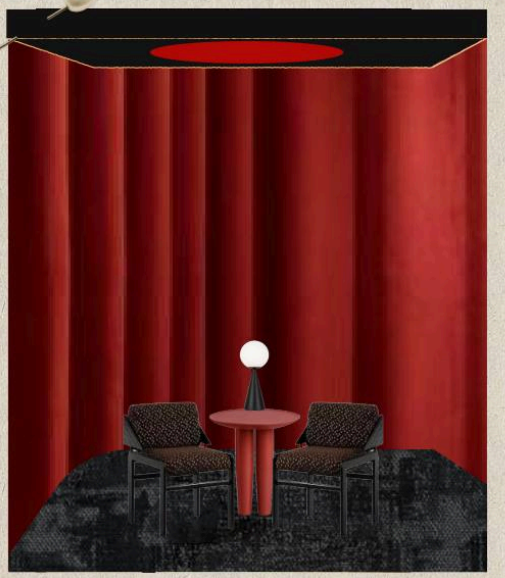

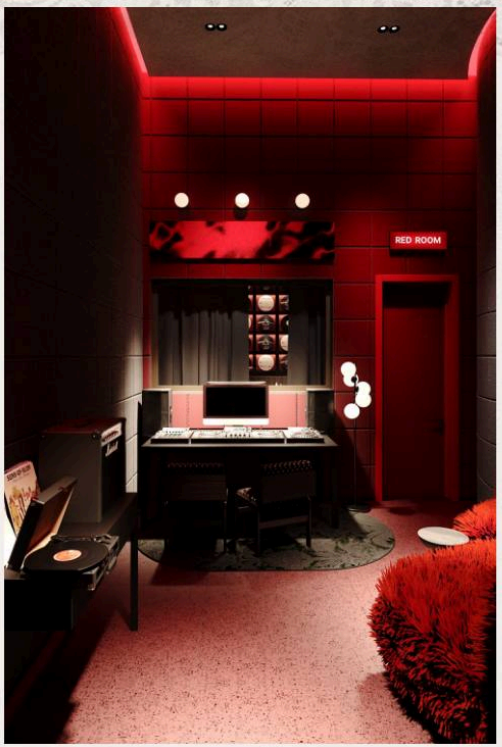

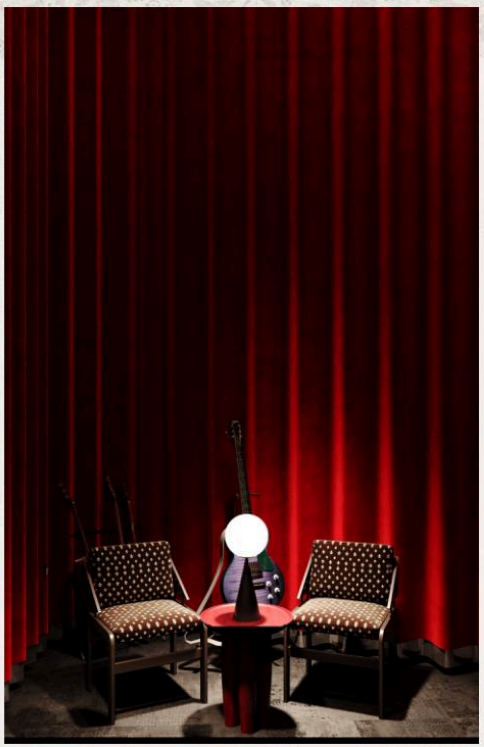

*Визуализации выполнены визуализаторами в рамках работы над проектом в Pergaev Bureau в 2026 г.

КОЛЛАЖ КАК ТЗ ВИЗУАЛИЗАТОРУ





*Визуализации выполнены визуализаторами в рамках работы над проектом в Pergaev Bureau в 2026 г.






*Визуализации выполнены визуализаторами в рамках работы над проектом в Pergaev Bureau в 2026 г.

ПОДАЧА ПОЛРАМНИКА

ФОРМИРОВАНИЕ ВЕЙ ГРАФИЧЕСКОЙ ИНФОРМАЦИИ ПРОЕКТА НА ПЛАНШЕТЕ ЗАДАННОГО ФОРМАТА


(4)

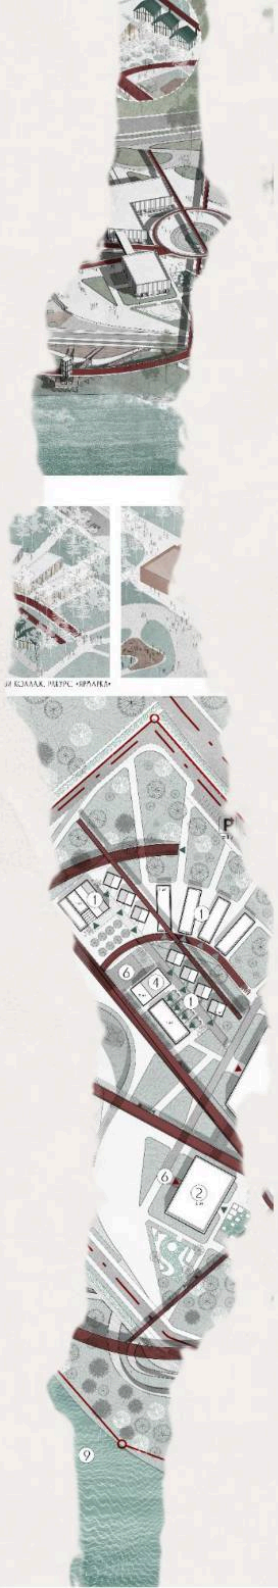

ПОДРАМНИК





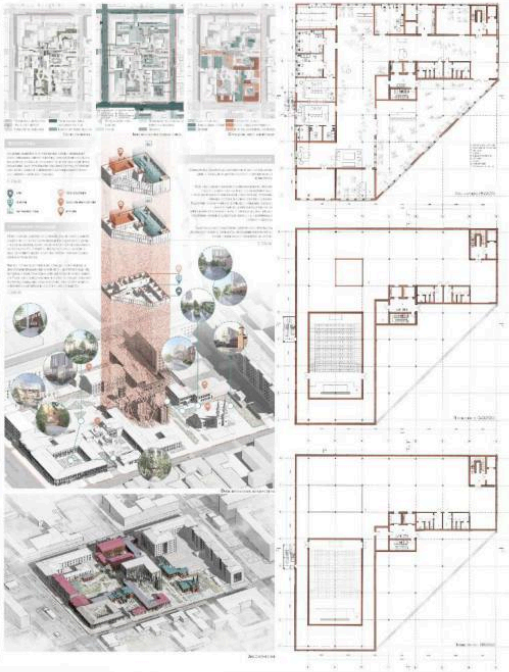







Бакалаврская дипломная работа "реконструкция квартала №420 в г. Уфе" 2024 год

ПОДРАМНИК

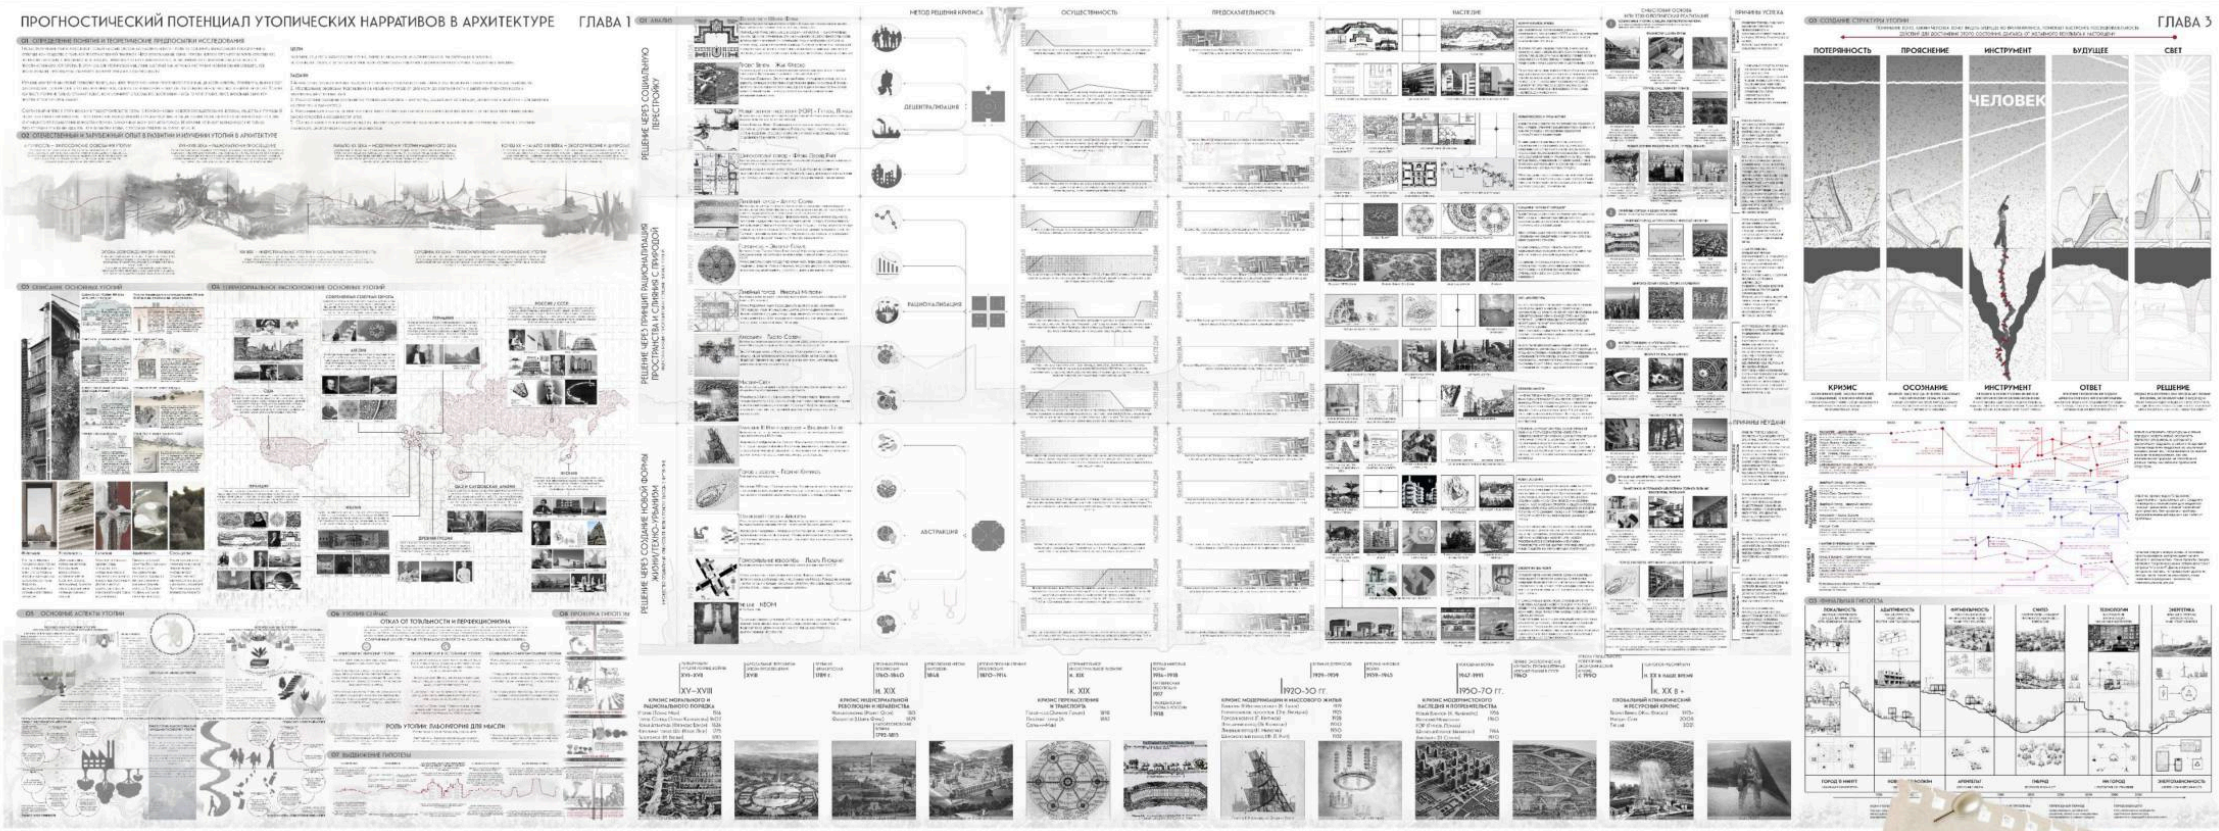

Магистерская дипломная работа "прогностический потенциал утопических нарративов в архитектуре" 2026 год

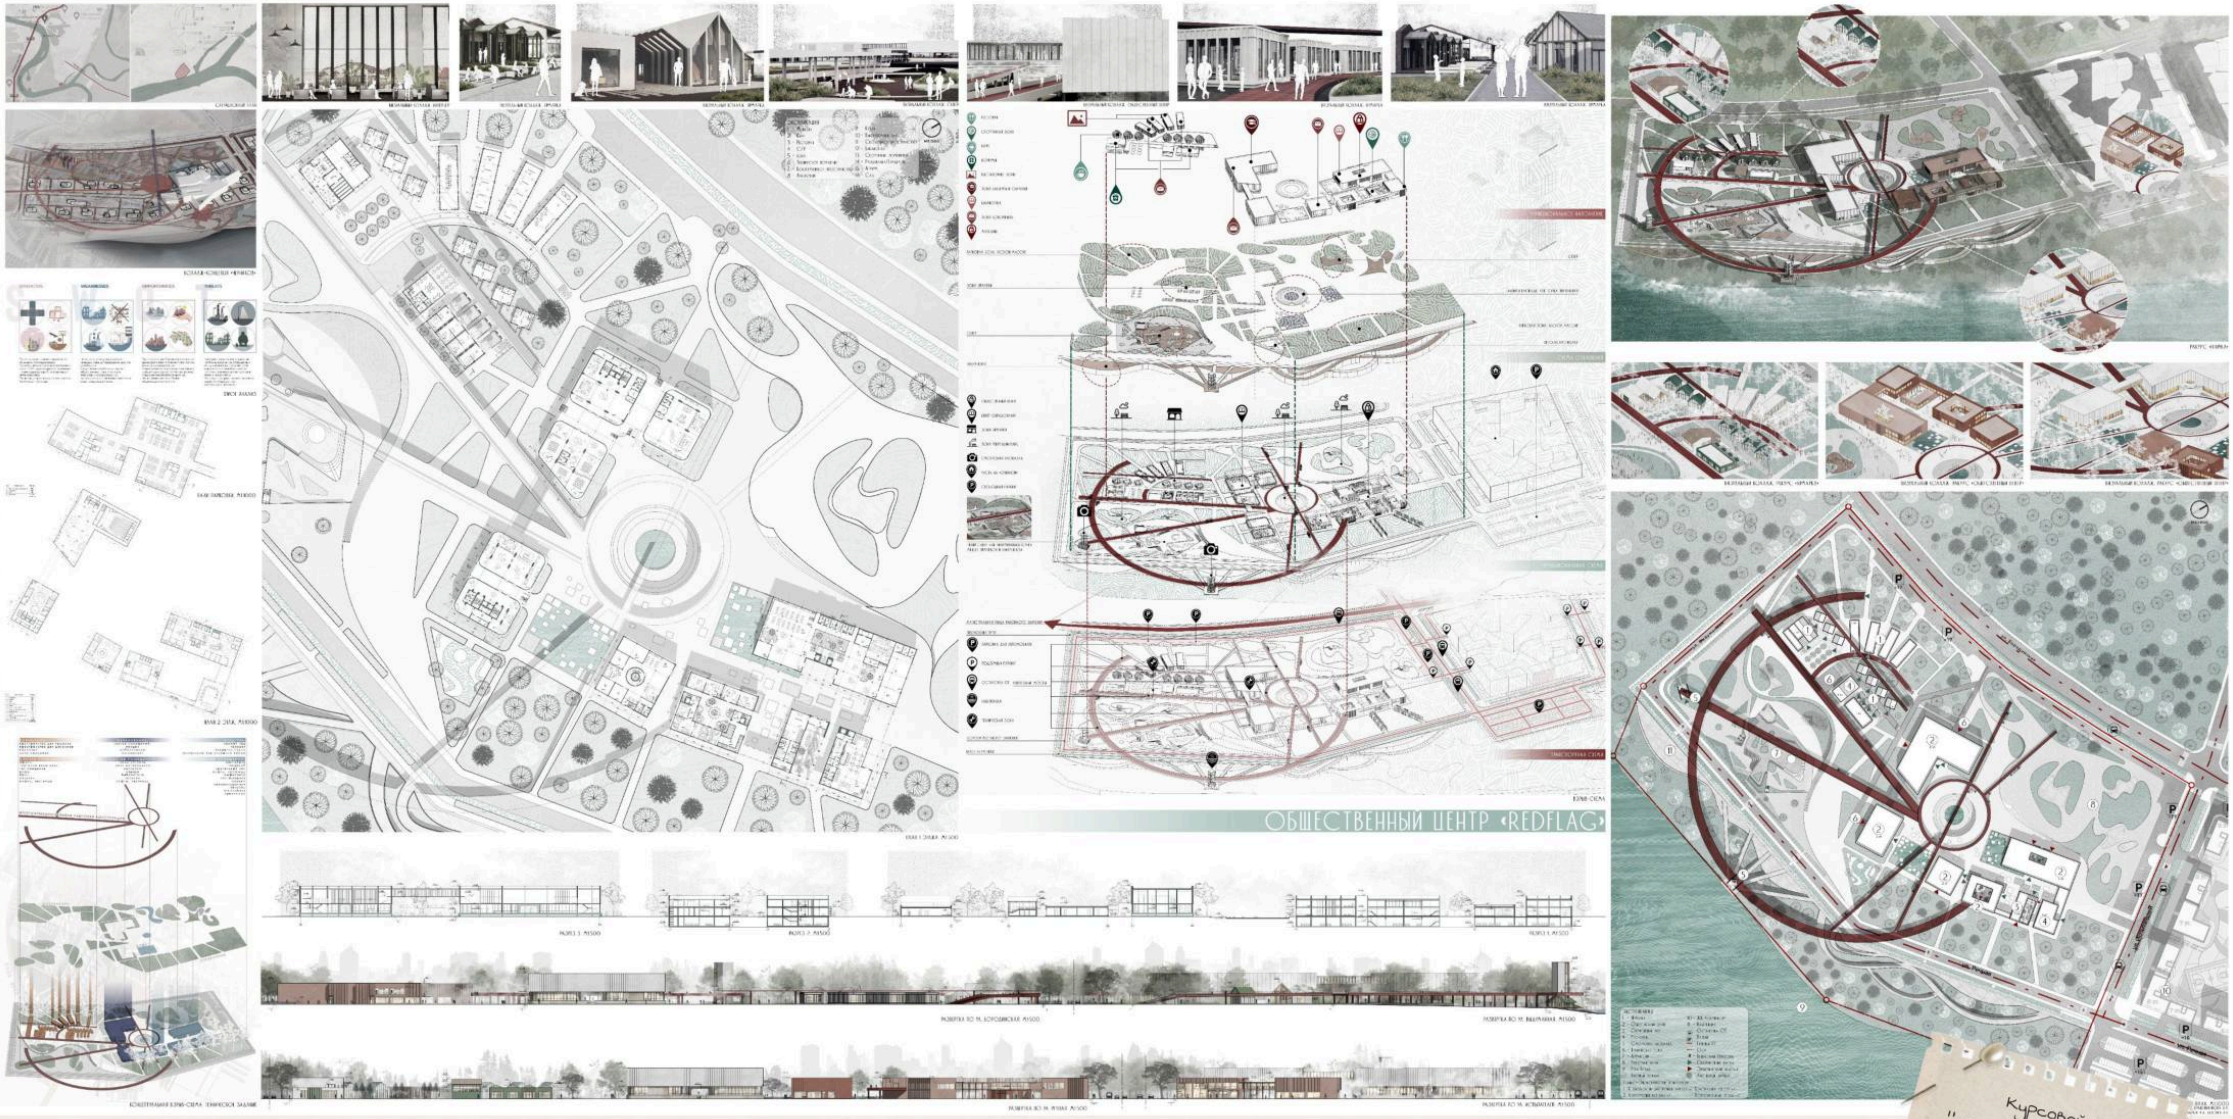


Курсовой проект
"общественный центр"
2023 год

Архитектурный рисунок


Выразить мысль рисунком


(5)

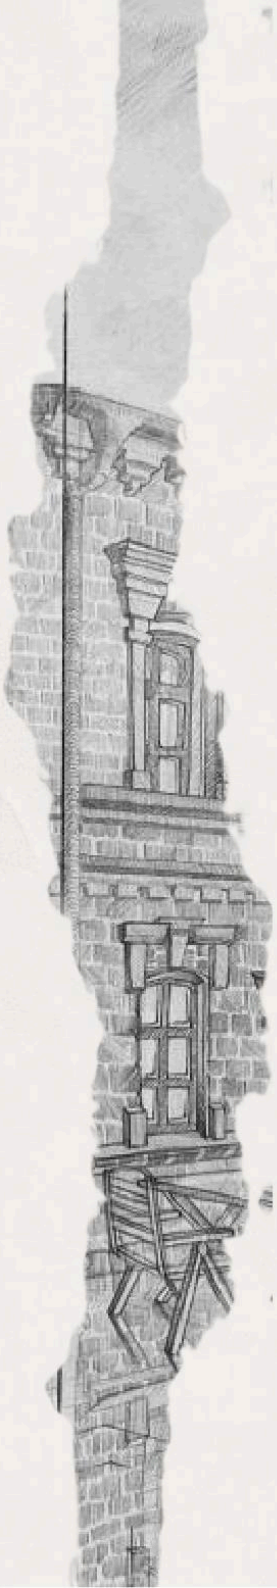


АРХИТЕКТУРНЫЙ РИСУНОК

*Данная работа участвовала в международном конкурсе

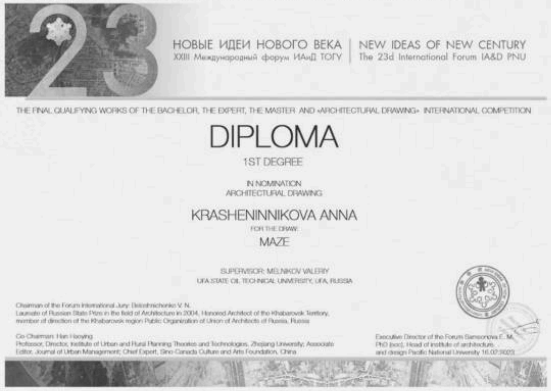
23
НОВЫЕ ИДЕИ НОВОГО ВЕКА | NEW IDEAS OF NEW CENTURY
XXIII Международный форум ИАиД ТОГУ | The 23d International Forum IA&D PNU
THE FINAL QUALIFYING WORKS OF THE BACHELOR, THE EXPERT, THE MASTER AND «ARCHITECTURAL DRAWING» INTERNATIONAL COMPETITION
DIPLOMA
1ST DEGREE
IN NOMINATION
ARCHITECTURAL DRAWING
KRASHENINNIKOVA ANNA
FOR THE DRAW:
MAZE
SUPERVISOR: MELNIKOV VALERIY
UFA STATE OIL TECHNICAL UNIVERSITY, UFA, RUSSIA
Chairman of the Forum International Jury: Dolzhnikhenko V. N.
Laureate of Russian State Prize in the field of Architecture in 2004, Honored Architect of the Khabarovsk Territory,
member of direction of the Khabarovsk region Public Organization of Union of Architects of Russia, Russia
Co-Chairman: Han Haoping
Professor, Director, Institute of Urban and Rural Planning Theories and Technologies, Zhejiang University; Associate
Editor, Journal of Urban Management; Chief Expert, Sino-Canada Culture and Arts Foundation, China
Executive Director of the Forum Samsonova E. M.
PhD (eco), Head of Institute of architecture
and design Pacific National University 16.07.2023

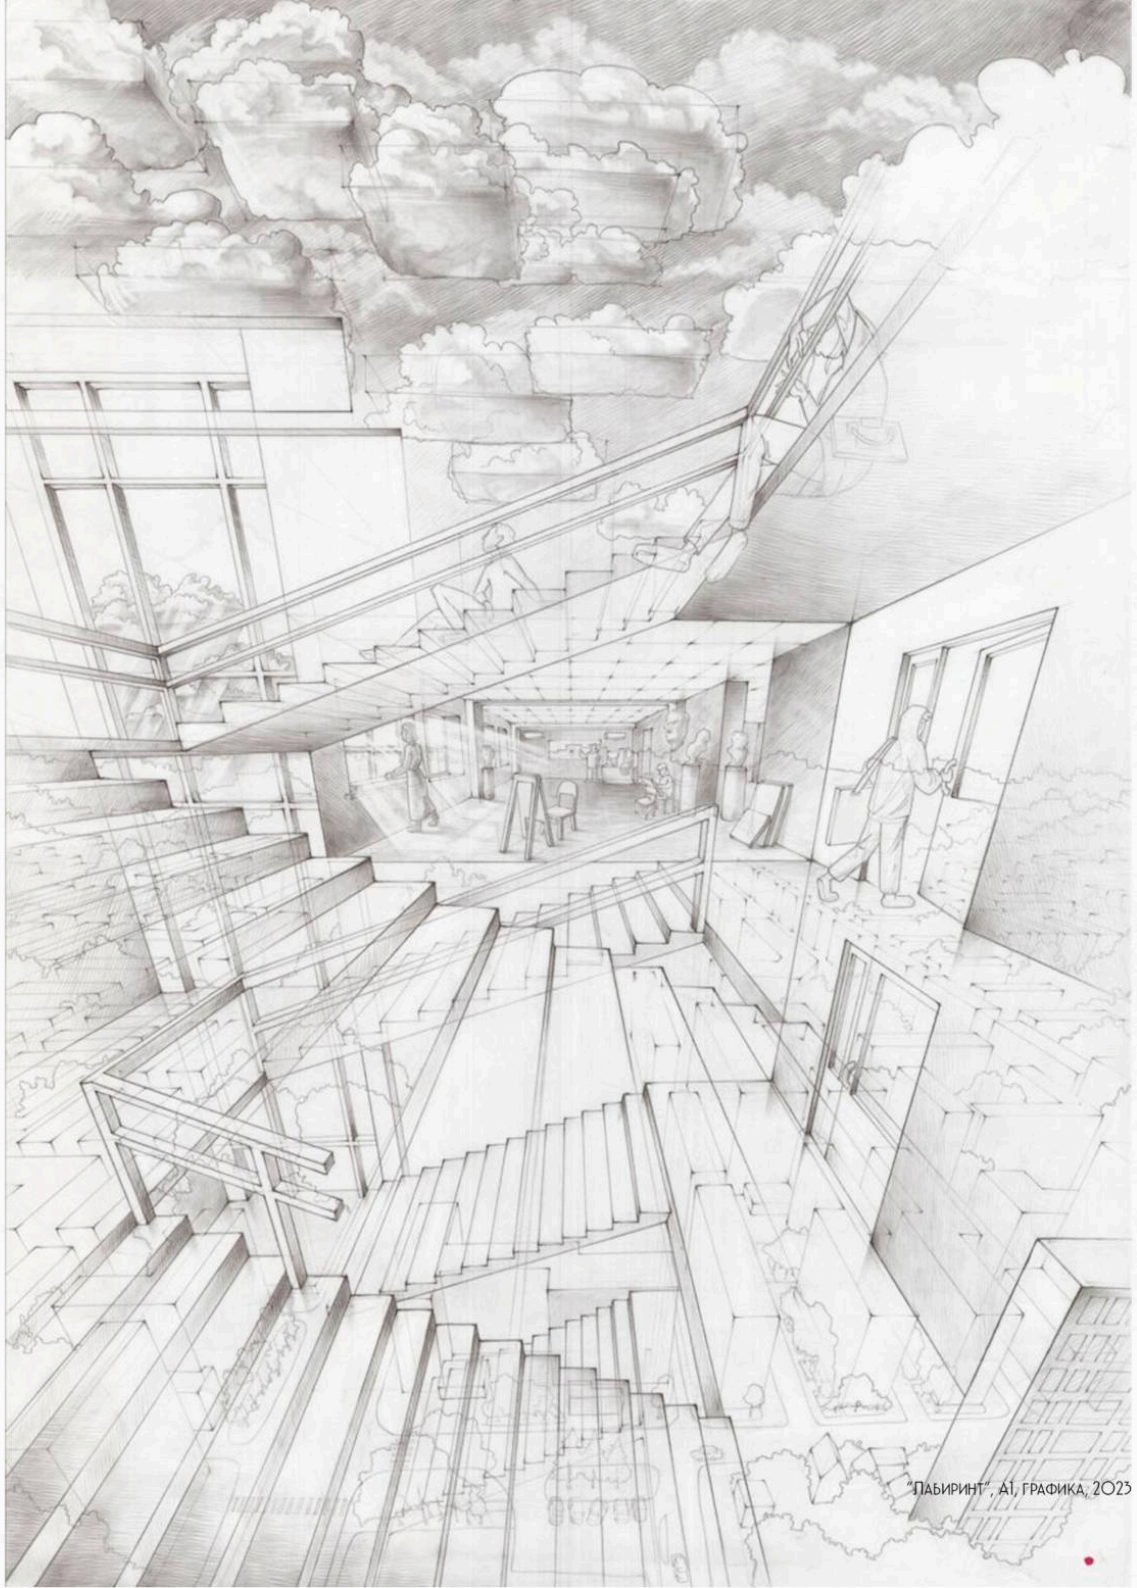


"Лабиринт", А1, графика, 2023

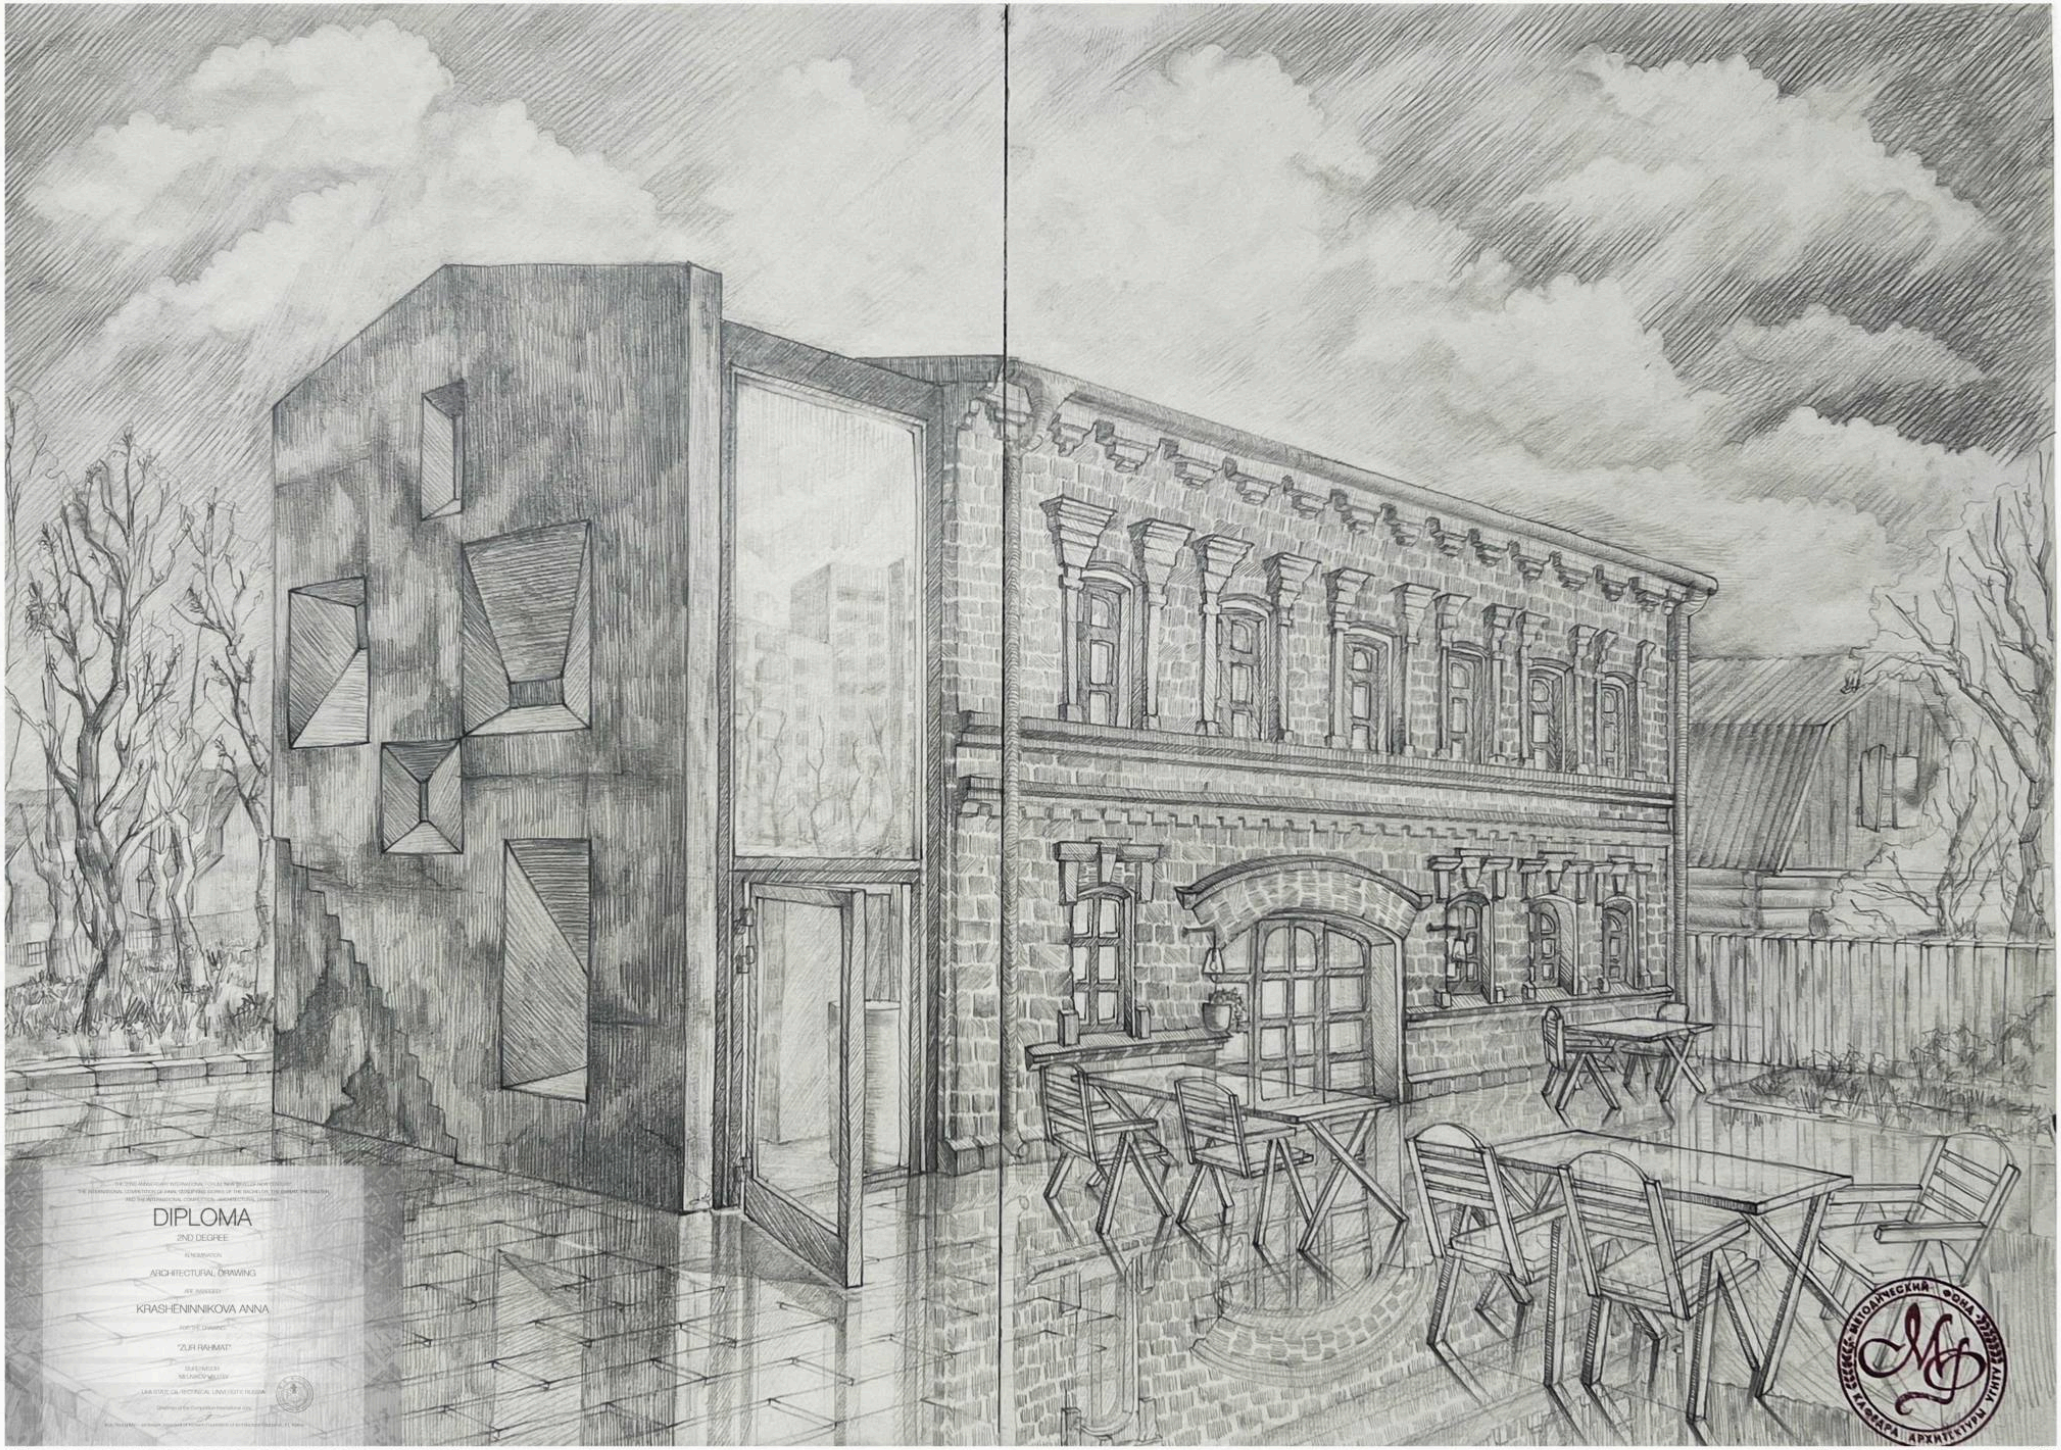


*Данная работа участвовала в международном конкурсе


"Зур-Рахмат", А2, графика, 2021

АРХИТЕКТУРНЫЙ РИСУНОК

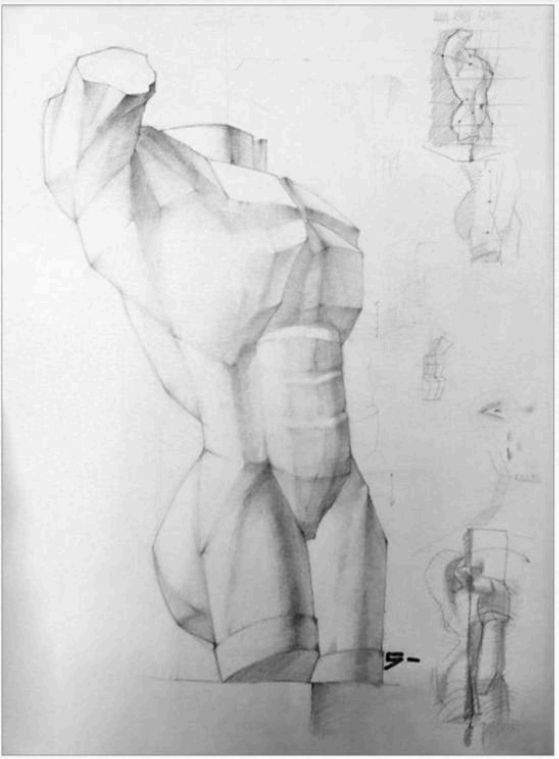

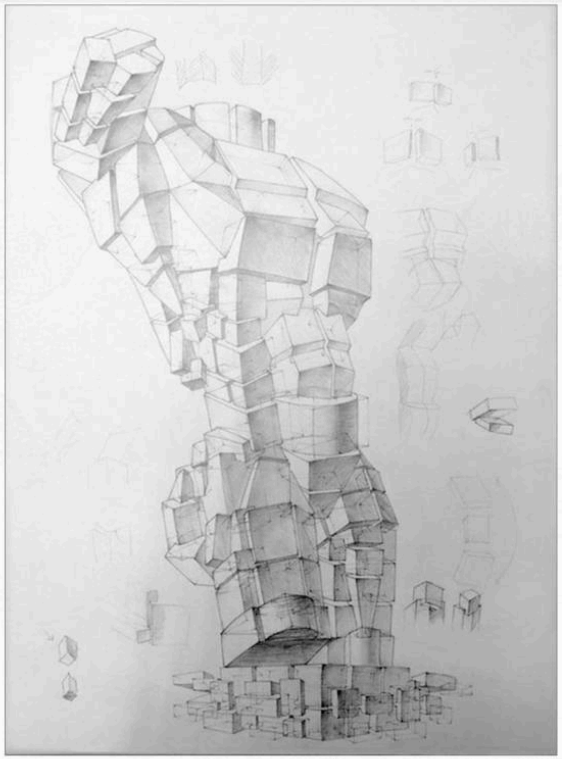

Трансформация "торс", графика, 75х55, 2022

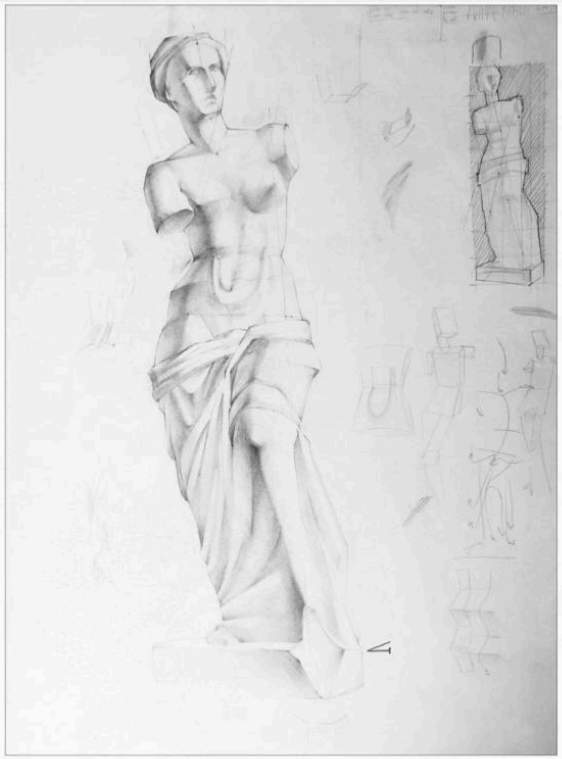



Трансформация "Венера", графика, 75х55, 2022